

POLITECNICO DI MILANO SCUOLA DEL DESIGN C.L. DESIGN DEGLI INTERNI PROGETTO:

QUINTA MONROY SIMPLEX STUDIO

STRUMENTI E METODI DEL PROGETTO

MARCO FERRARA
STUDENTI:

ISABELLA RUINA

POÄNG\_391-256-69 PROSPETTI E SEZIONI

NOME FILE:


POÄNG\_391-256-69.dwg

A720

2017.05.23

DATA: 2017/04/03 SCALA:1:5 / 1:10
REV: A FORMATO: A1

10 110cm 125cm 50cr

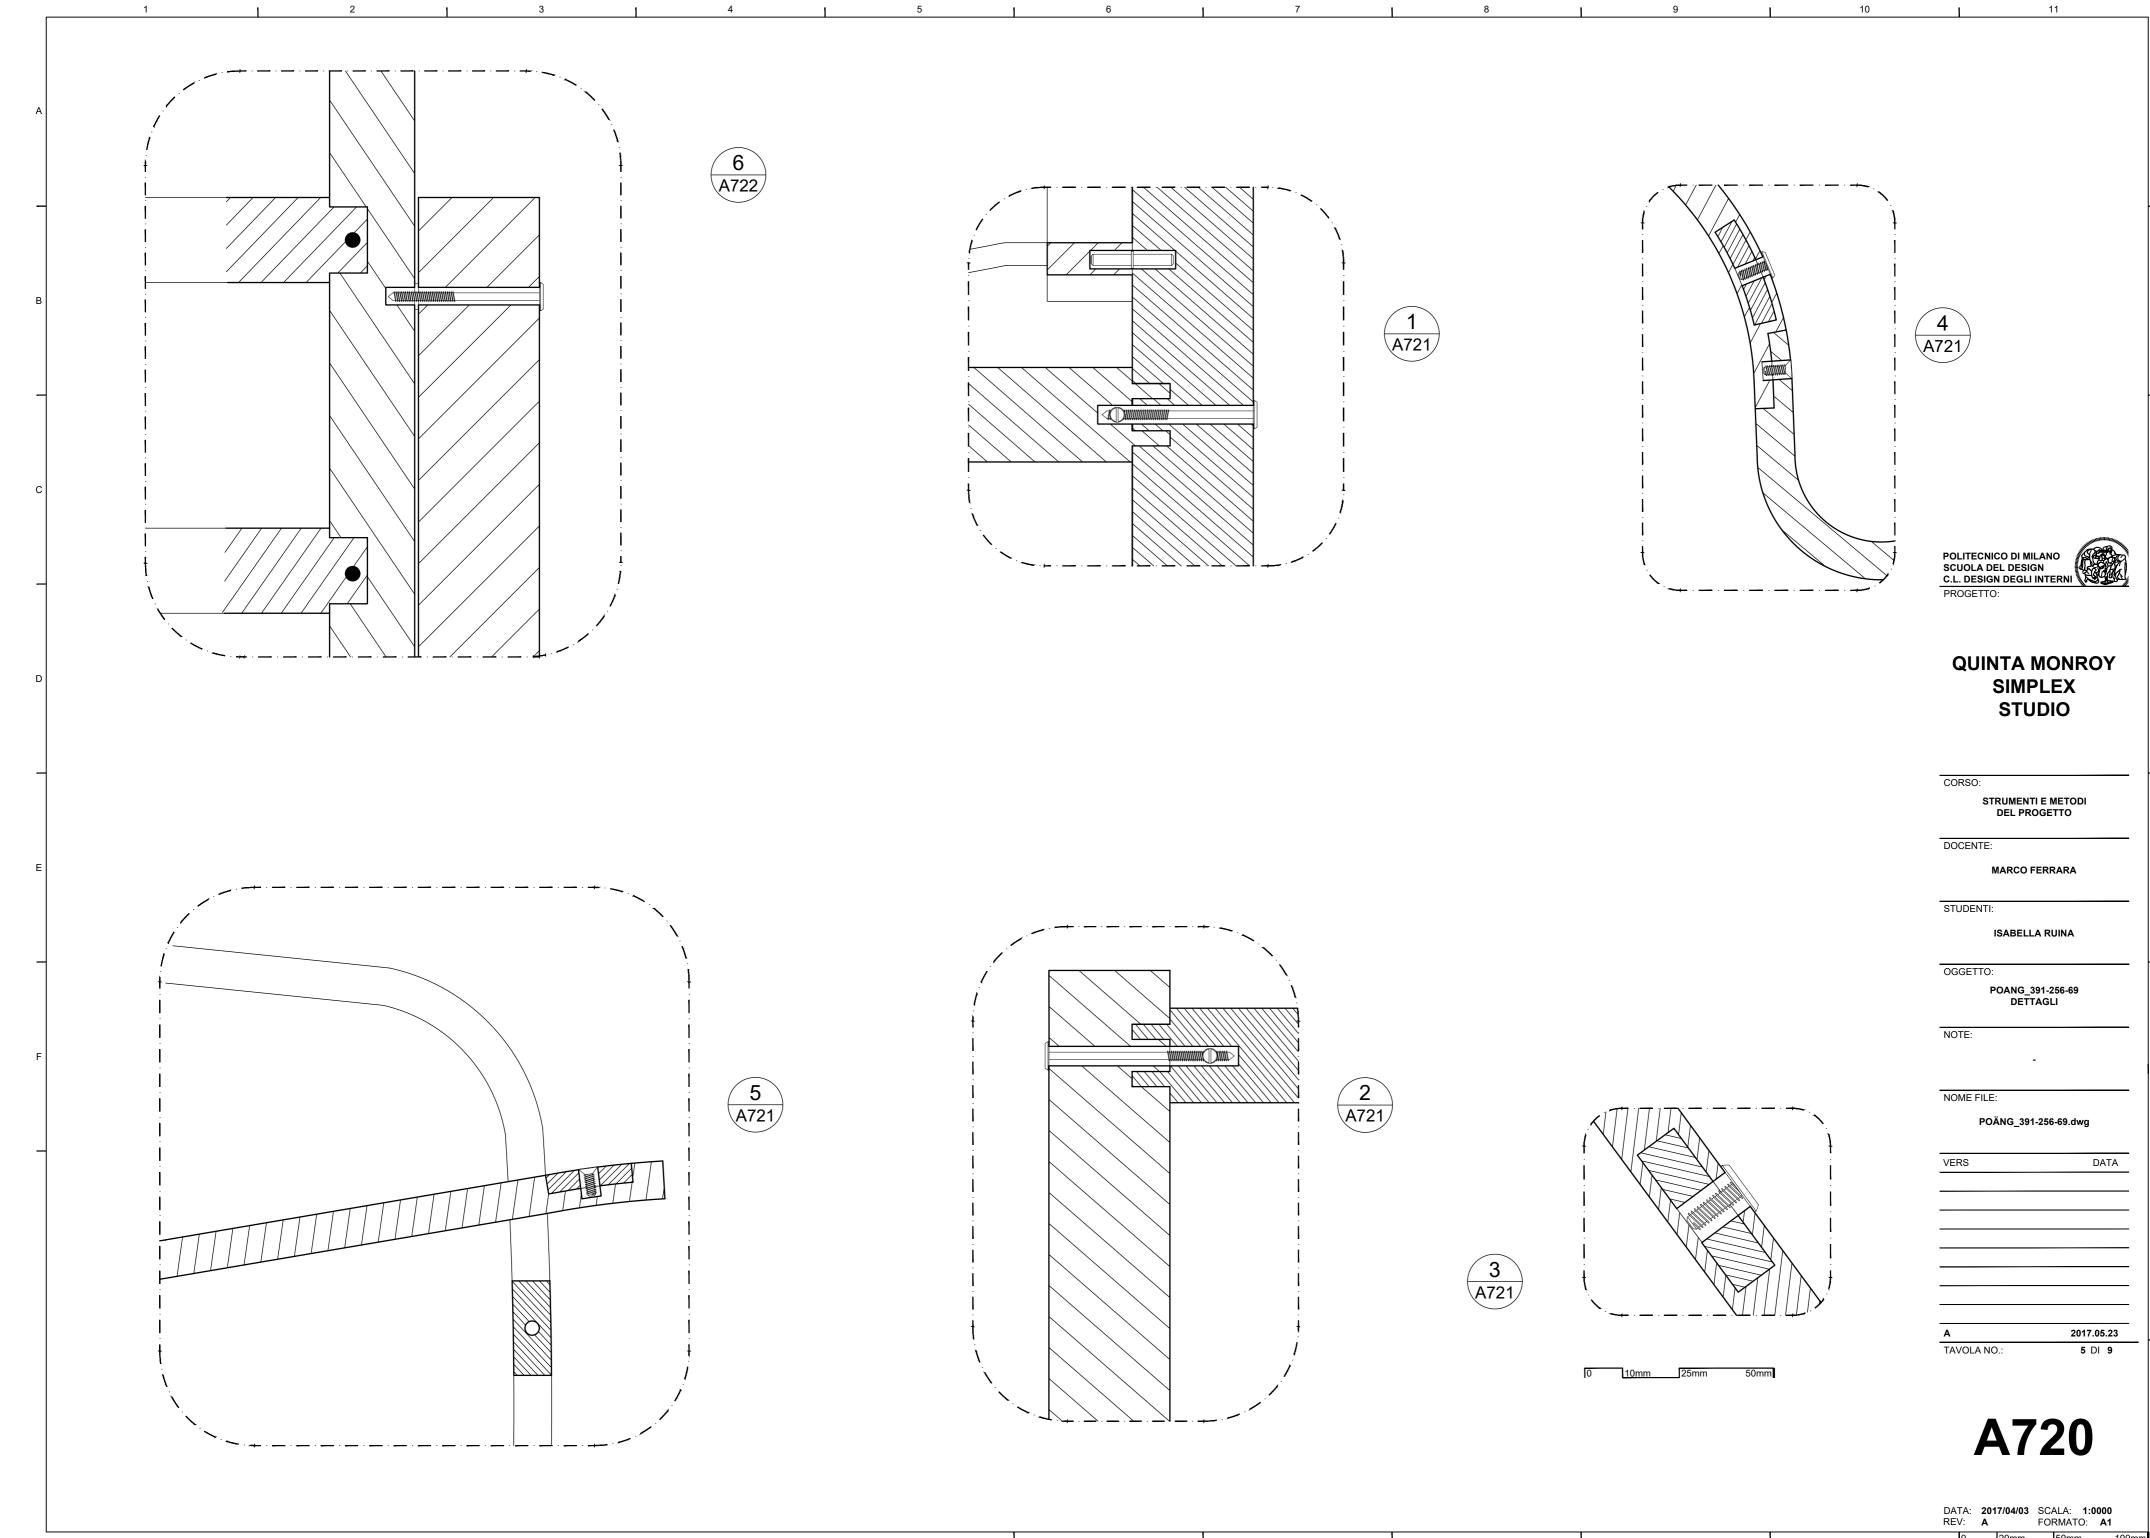

0 20mm 50mm