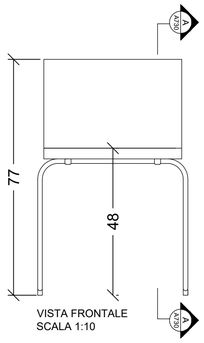

VISTA FRONTALE
SCALA 1:10

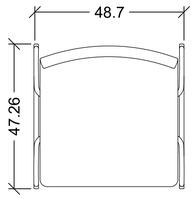

VISTA DALL'ALTO
SCALA 1:10

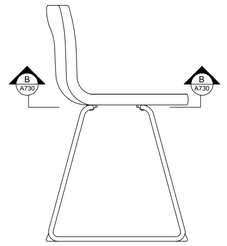

VISTA LATERALE
SCALA 1:10

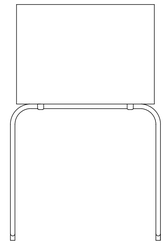

VISTA DAL DIETRO
SCALA 1:10

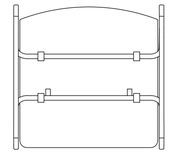

VISTA DAL BASSO
SCALA 1:10

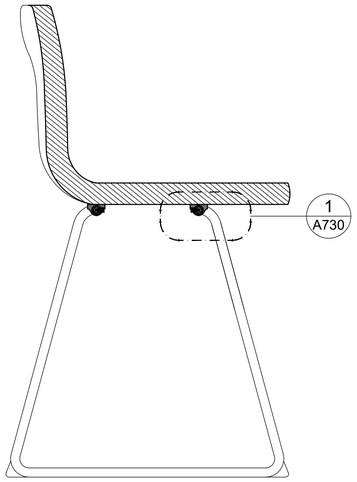

SEZIONE AA
SCALA 1:5

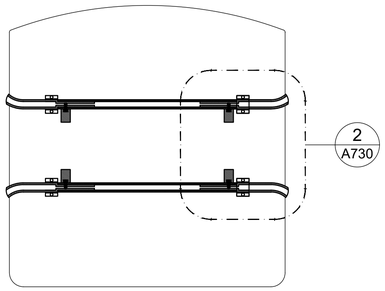

SEZIONE BB
SCALA 1:5

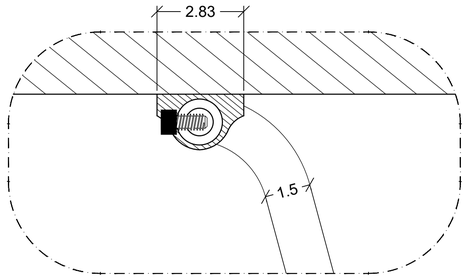

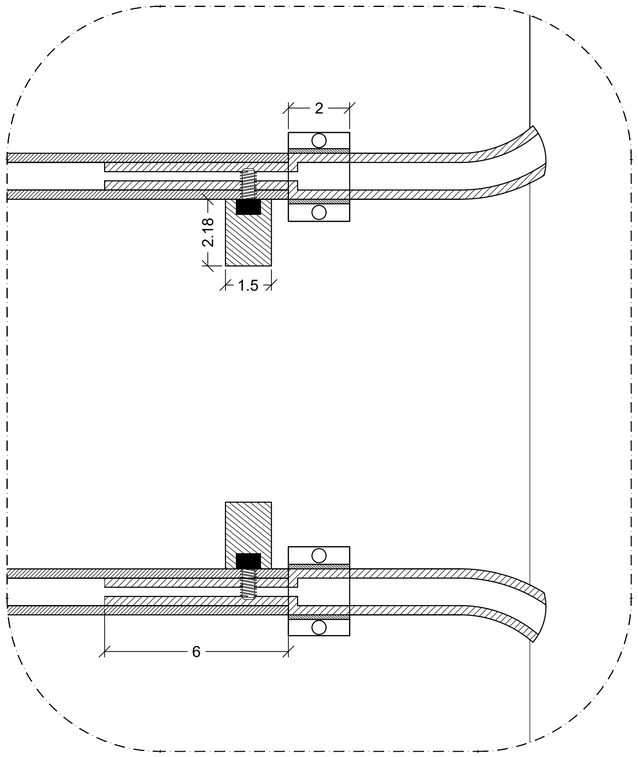

SCALA 1:1

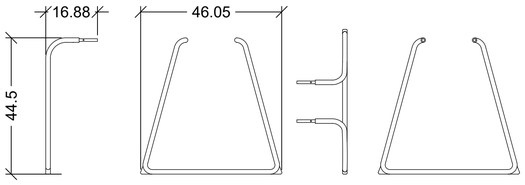

VISTA LATERALE VISTA DAL DIETRO VISTA DALL'ALTO VISTA FRONTALE

4x 100176

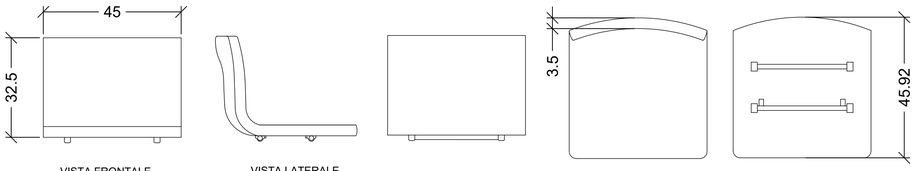

VISTA FRONTALE VISTA LATERALE VISTA DAL DIETRO VISTA DALL'ALTO VISTA DAL SOTTO

POLITECNICO DI MILANO
SCUOLA DEL DESIGN
C.L. DESIGN DEGLI INTERNI

PROGETTO:

QUINTA MONROY SIMPLEX STUDIO

CORSO:
STRUMENTI E METODI DEL PROGETTO

DOCENTE:
MARCO FERRARA

STUDENTI:
ISABELLA RUINA

OGGETTO:
SEDIA BERNHARD_201-638-02 PROSPETTI, SEZIONI E DETTAGLI

NOTE:
-

NOME FILE:
BERNHARD_201-638-02.dwg

VERS	DATA
A	2017.05.23

TAVOLA NO.: **9** DI **12**

A730

DATA: **2017/04/03** SCALA: **1:5 / 1:10**
REV: **A** FORMATO: **A1**

DIRECTORY : C:\USERS\ISA\ONEDRIVE\FERRARA\FASE 2\QM-S_1_STUDIO\BERNHARD_201-638-02\BERNHARD_201-638-02.DWG | PLOTTED ON: 30/05/2017 01:45:07 | BY USER: ISABELLA RUINA